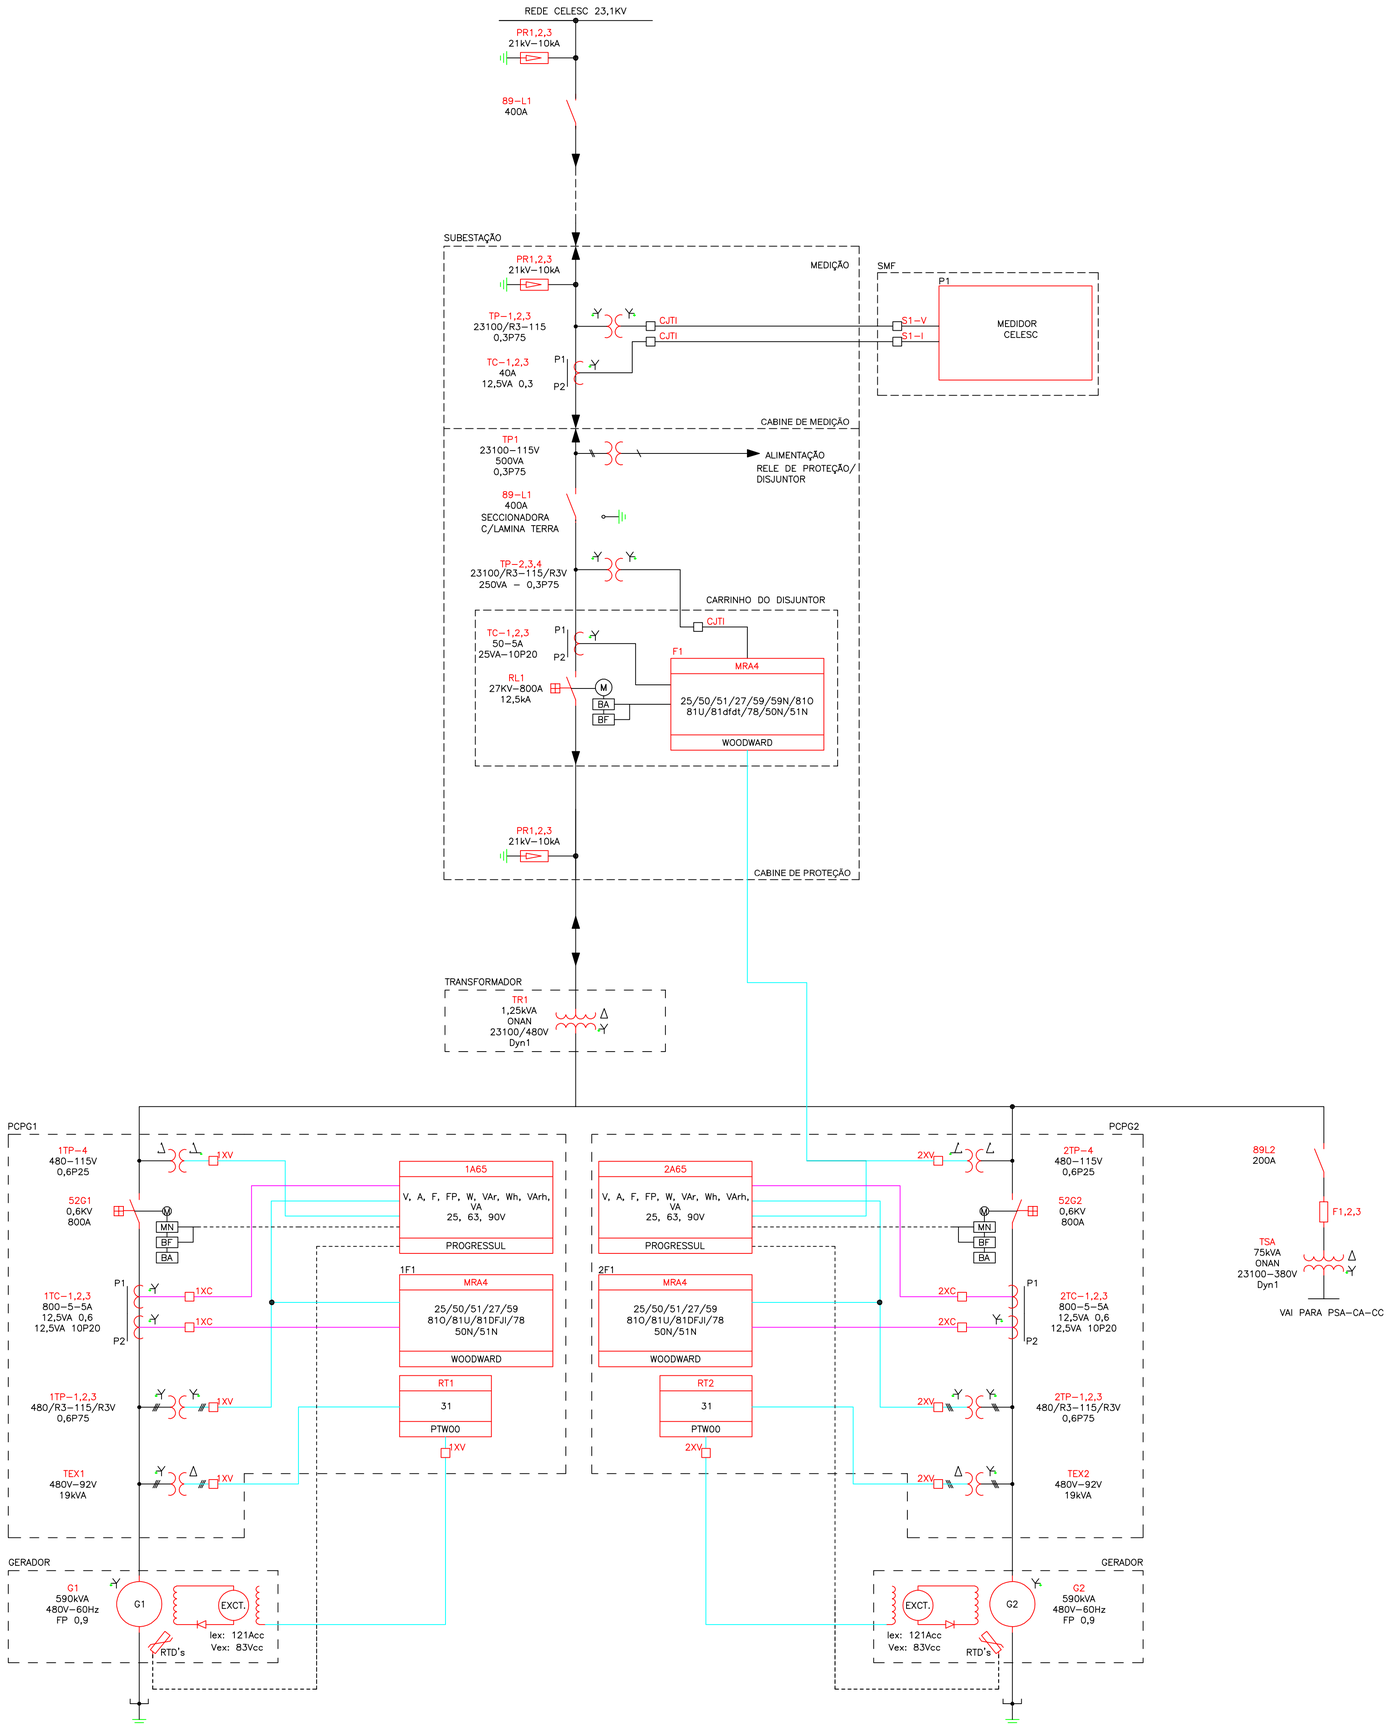


LEGENDA DE TAG'S:

PMF – PAINEL DE MEDIÇÃO DE FATURAMENTO
CSPSE – CUBÍCULO DE SAÍDA E PROTEÇÃO DA SUBESTAÇÃO
PSCP–G1 E PSCP–G2 – PAINEL DE CONTROLE E PROTEÇÃO DO GERADOR

PROTEÇÃO:

25 – RELÉ DE VERIFICAÇÃO DE SINCRONISMO OU SINCRONIZAÇÃO
27 – RELÉ DE SUBTENSÃO
31 – DISPOSITIVO DE EXCITAÇÃO
32 – RELÉ DIRECIONAL DE POTÊNCIA
40 – RELÉ DE PERDA DE EXCITAÇÃO OU RELÉ DE PERDA DE CAMPO
49 – RELÉ TÉRMICO
50 – RELÉ DE SOBRECORRENTE INSTANTÂNEO
51 – RELÉ DE SOBRECORRENTE TEMPORIZADO
52 – DISJUNTOR DE CORRENTE ALTERNADA
59 – RELÉ DE SOBRETENSÃO
60 – RELÉ DE BALANÇO DE CORRENTE OU TENSÃO
62 – RELÉ TEMPORIZADOR
64 – RELÉ DETETOR DE TERRA
65 – REGULADOR
67 – RELÉ DIRECIONAL DE SOBRECORRENTE
72 – DISJUNTOR DE CORRENTE CONTÍNUA
78 – SALTO VETORIAL
81 – RELÉ DE FREQUÊNCIA (SUB OU SOBRE)
86 – RELÉ AUXILIAR DE BLOQUEIO
87 – RELÉ DE PROTEÇÃO DIFERENCIAL
89 – CHAVE SECCIONADORA
50N – SOBRECORRENTE INSTANTÂNEO DE NEUTRO
51N – SOBRECORRENTE TEMPORIZADO DE NEUTRO
50G – SOBRECORRENTE INSTANTÂNEO DE TERRA
51G – SOBRECORRENTE TEMPORIZADO DE TERRA
50BF – RELÉ DE PROTEÇÃO CONTRA FALHA DE DISJUNTOR (TAMBÉM CHAMADO DE 50/62 BF)
51Q – RELÉ DE SOBRECORRENTE TEMPORIZADO DE SEQÜÊNCIA NEGATIVA COM TEMPO DEFINIDO
51V – RELÉ DE SOBRECORRENTE COM RESTRIÇÃO DE TENSÃO
51C – RELÉ DE SOBRECORRENTE COM CONTROLE DE TORQUE
59Q – RELÉ DE SOBRETENSÃO DE SEQÜÊNCIA NEGATIVA
59N – RELÉ DE SOBRETENSÃO RESIDUAL OU SOBRETENSÃO DE NEUTRO

MEDIÇÃO:

V – TENSÃO
I – CORRENTE
F – FREQUÊNCIA
FP – FATOR DE POTÊNCIA
kW – POTÊNCIA ATIVA
kVAr – POTÊNCIA REATIVA
kVA – POTÊNCIA APARENTE
kWh – ENERGIA ATIVA
kVArh – ENERGIA REATIVA

SIMBOLOGIA

1BT2 – CHAVE DE AFERIÇÃO
CHAVE FACA UNIPOLAR
DISJUNTOR TRIPOLAR
SECCIONADORA TRIPOLAR
P1 / P2 – TRANSFORMADOR DE CORRENTE
TRANSFORMADOR DE POTENCIAL
TRANSFORMADOR DE POTÊNCIA
G1 / EXCT. – GERADOR

CABO OU BARRAMENTO DE FORÇA
CABO SINAIS DE CORRENTE
CABO SINAIS DE TENSÃO

REVISÃO	DATA	DESCRIÇÃO	ELABORADO
03	29/11/2019	REVISÃO GERAL	GHS
02	22/11/2019	REVISÃO GERAL	GHS
01	17/10/2019	REVISÃO GERAL	GHS

Progressul Sistemas de Energia

OBRA: CGH BOTELHO			LOGO CLIENTE: ESTELAR
CLIENTE: BOTELHO GERADORA DE ENERGIA LTDA			
LOCALIDADE: JARAGUÁ DO SUL - SC			
TÍTULO: ARRANJO GERAL DIAGRAMA UNIFILAR			ART DO PROJETO: -
			DESENHO: -
ELABORADO: TIMÓTHEO F. MÜLLER	VERIFICADO: ANDRÉ L. S. DE JESUS		APROVADO: ANDRÉ L. S. DE JESUS
Nº DOCUMENTO: PR040030-DU-001	REVISÃO: 03	ESCALA: S/E	DATA: 31/07/2019
			FOLHAS: 1 DE 1
CLIENTE: BOTELHO GERADORA DE ENERGIA LTDA CNPJ: 11.220.193/0001-02		RESP. TÉCNICO: ANDRÉ LUÍS SOUZA DE JESUS CREA-SC 101236-2	